# KITCHEN PLAN

SOURCE COORDINATION / 22 OCT 2026

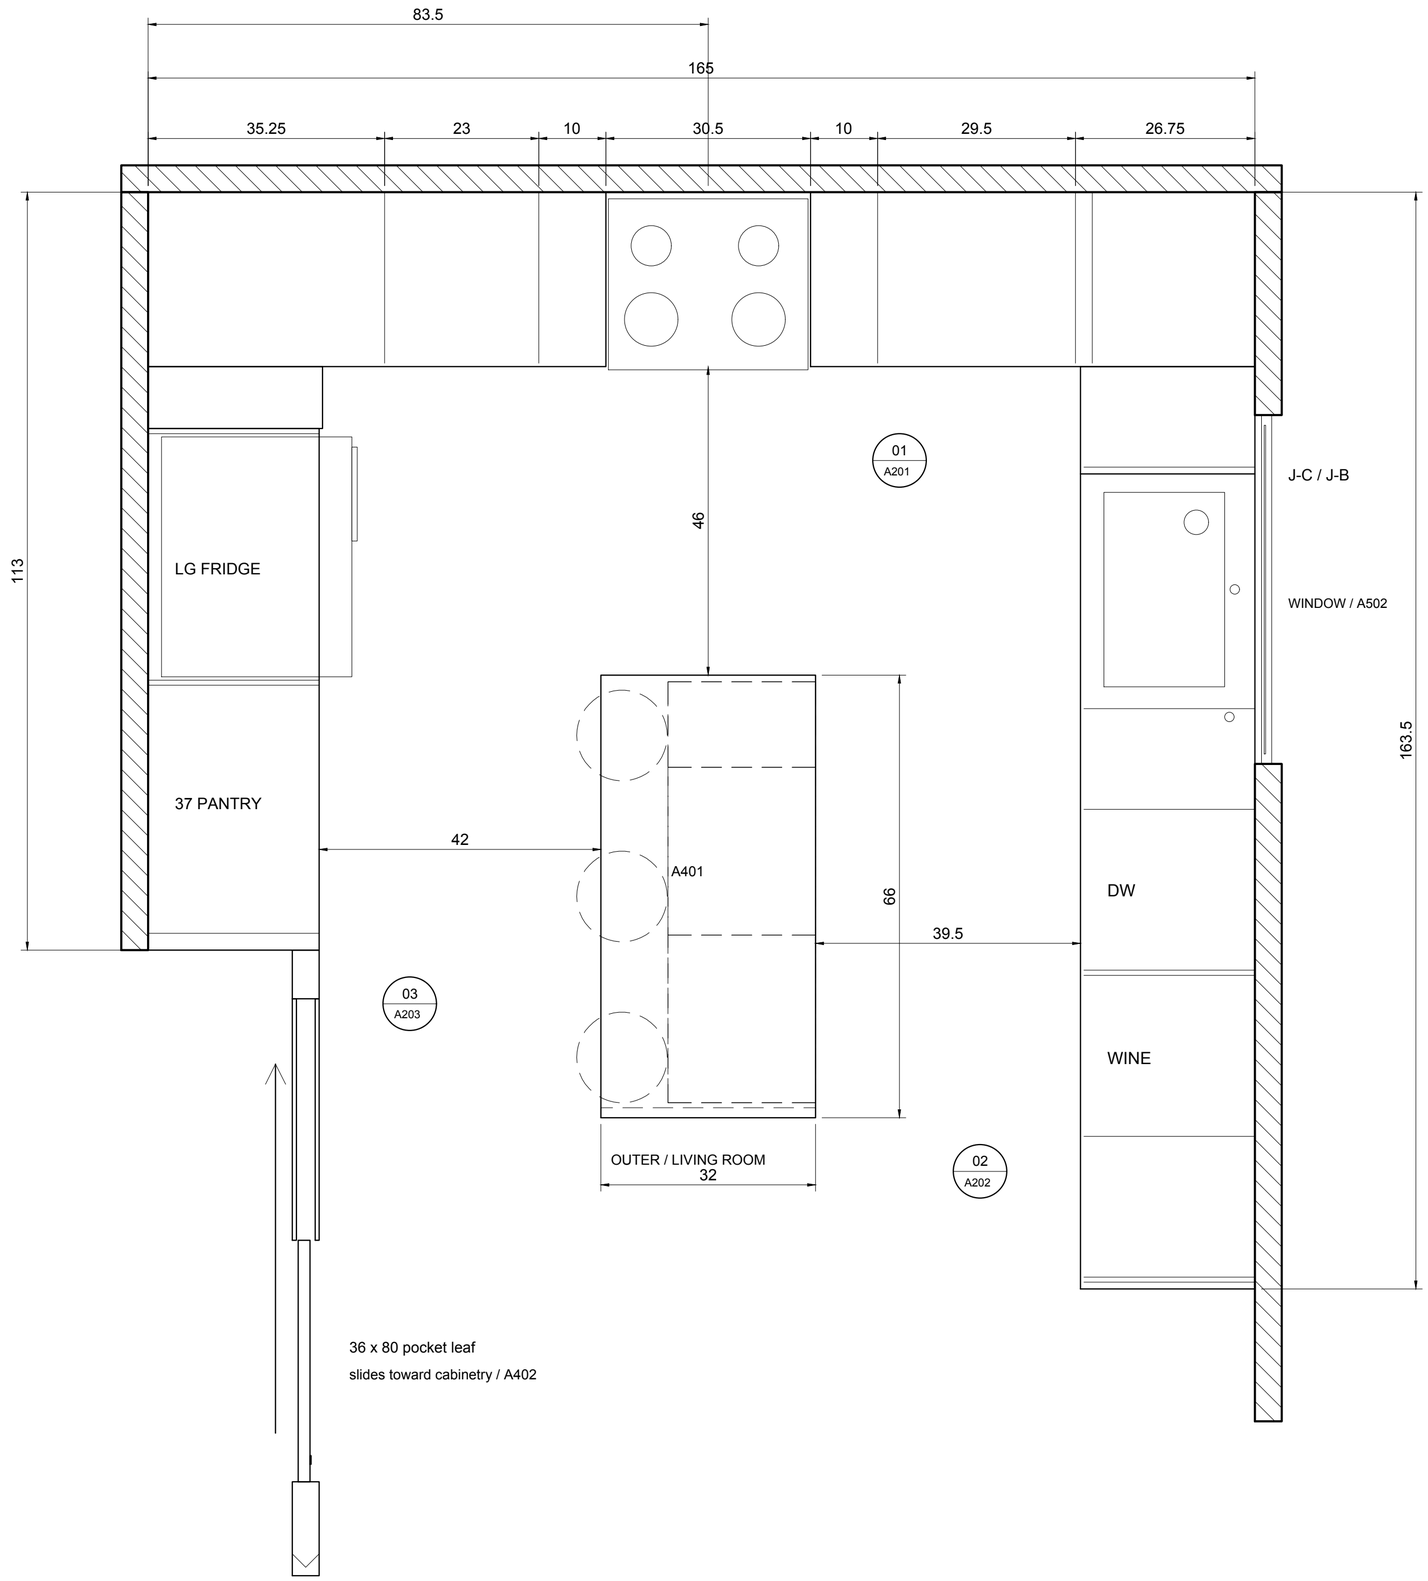


## COORDINATION DATUMS

Origin: back-left finished drywall.
X across range wall; plan depth D to living room.
Native WCS Y = -D; Z = height. Ceiling = 108.
Range and island centreline X = 83.5.

COUNTERTOPS
12 mm Statuario porcelain throughout.
36 finished height; 26 perimeter depth.
Island: 66 x 32; body 22 + overhang 10.
One waterfall at outer / living-room end.

DIMENSION CHAIN
165 = 35.25 + 23 + 10 + 30.5
+ 10 + 29.5 + 2.5 + 24.25
113 = 35.25 + .75 + 36.75
+ .75 + 37 + 2.5

FIXED SURFACE GAPS
Left side 42; sink side 39.5; rear 46.
These exclude occupants and open doors.

SOURCE / HOLDS
Cabinet pp. 2-6; Stone R9 S02.
Window CL / sink / tap: 59.25 nominal.
Source 1/4 in. discrepancy: field verify.
Pocket kit and wall construction unselected.
Wall thickness and adjacent extent contextual.
Three stools: compact occasional seating.

KITCHEN RENOVATION

DESIGN COORDINATION STUDY - FIELD VERIFY - NOT FOR CONSTRUCTION

Kitchen plan

22 OCT 2026 | 3/4 in. = 1 ft | 24 x 18 in. | INCHES

A101